

SUPPLY SCOPE: Nudura ICF forms, accessories, pre-cut service, alignment hire and haulage as the quotation. SCOTLAND - Building Standards (Scotland). Height ~6.3 m above the ground floor, below 11 m. Basement waterproofing (BS 8102), pool tank, slabs, vaulted roof, glazing and partitions are shown in good faith for coordination only - engineer / specialists to design.

QUOTATION - NOT FOR CONSTRUCTION

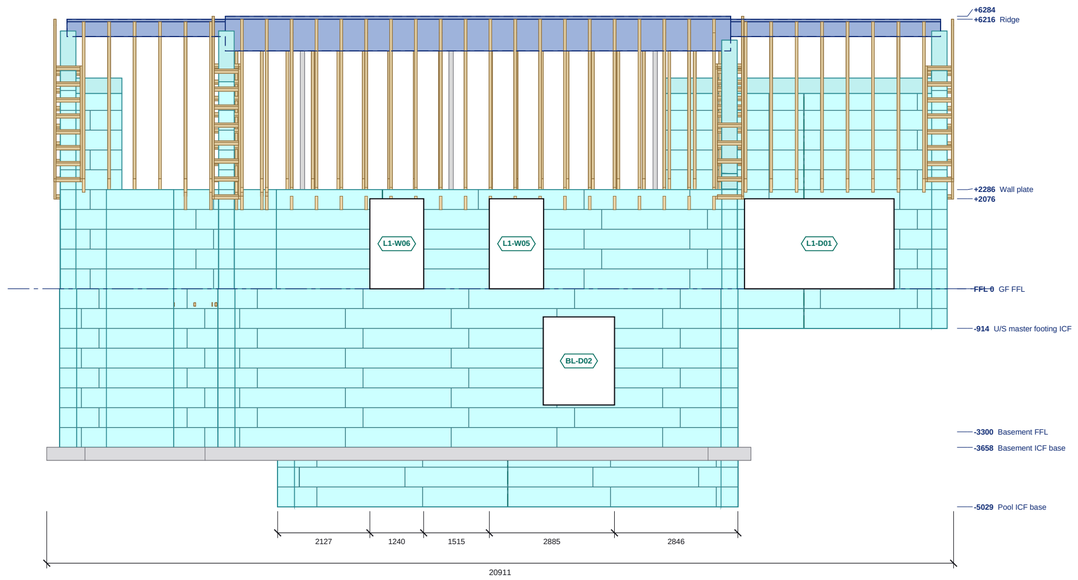

EAST ELEVATION

Scale 1:100 @ A2 | Levels above GF FFL; sills and heads in the schedule

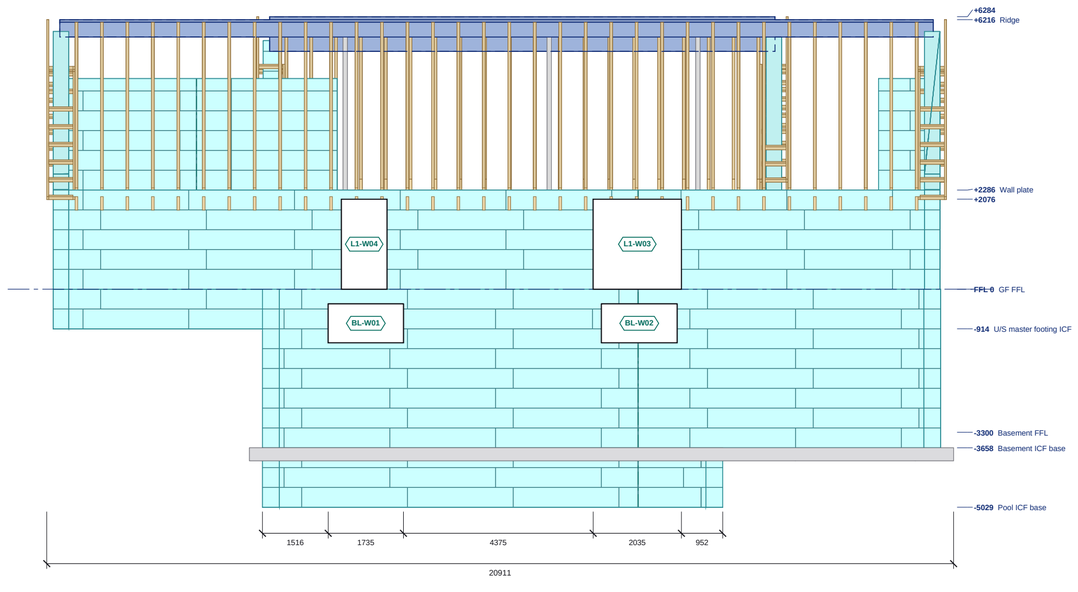

WEST ELEVATION

Scale 1:100 @ A2 | Levels above GF FFL; sills and heads in the schedule

0 1 2 3 4 5m

ICF external EPS face
Block course joint
Stack joint
Roof build-up (slab / earth / sedum)

ELEVATION SCHEDULES

EAST ELEVATION: OPENINGS

Ref	Width	Height	Sill	Head	Lintel
BL-D02	1640	2030	-2680	+-650	-
L1-W05	1250	2075	0	+2075	-
L1-W06	1240	2075	0	+2075	-
L1-D01	3445	2075	0	+2075	-

Structural openings in the ICF; sill and head above GF FFL.

WEST ELEVATION: OPENINGS

Ref	Width	Height	Sill	Head	Lintel
BL-W01	1735	897	-1236	+-339	-
BL-W02	1745	897	-1236	+-339	-
L1-W03	2035	2075	0	+2075	-
L1-W04	1050	2075	0	+2075	-

Structural openings in the ICF; sill and head above GF FFL.

EAST ELEVATION: LEVELS

Level	FFL
Pool ICF base	-5029
Basement ICF base	-3658
Basement FFL	-3300
U/S master footing ICF	-914
GF FFL	0
top of ICF	+2076
Wall plate	+2286
Ridge	+6216
top of roof build-up	+6284

WEST ELEVATION: LEVELS

Level	FFL
Pool ICF base	-5029
Basement ICF base	-3658
Basement FFL	-3300
U/S master footing ICF	-914
GF FFL	0
top of ICF	+2076
Wall plate	+2286
Ridge	+6216
top of roof build-up	+6284

NOTES

1. ICF: Nudura 10" Std, 66.7 EPS + 254.0 core + 66.7 EPS = 387.4; 6" XR35, 101.6 EPS + 152.4 core + 101.6 EPS = 355.6. External EPS face shown with the block course joints, vertical block joints and stack joints as populated.
2. Levels above GF FFL. Openings are structural openings in the ICF; glazing, doors, render and finishes by others, not shown.
3. Roof build-up shown as modelled.
4. See ES26-084-GA-01 for plan setting out, lintels and steel.

REVISIONS

REV	DATE	DESCRIPTION
Q01	20.10.26	First issue - proposal Rev A

Nudura™ BuildEase

CLIENT	PROJECT
Mr K & Mrs Burrell	New Dwelling, Plot 1 Rivendell Park, Douglas

DRAWING TITLE
EAST AND WEST ELEVATIONS
ICF elevations with openings, levels and roof build-up

SCALE	SIZE	DATE
1:100	A2	20.10.26
DRAWN	CHECKED	APPROVED
TS		

STATUS	DRAWING No.	REV
QUOTATION	ES26-084-EL-02	Q01

Do not scale. All dimensions in millimetres, levels in metres from GF FFL. Check all dimensions on site.