
SUPPLY SCOPE: Nudura ICF forms, accessories, pre-cut service, alignment hire and haulage as the quotation. SCOTLAND - Building Standards (Scotland). Height ~6.3 m above the ground floor, below 11 m. Basement waterproofing (BS 8102), pool tank, slabs, vaulted roof, glazing and partitions are shown in good faith for coordination only - engineer / specialists to design.

QUOTATION - NOT FOR CONSTRUCTION

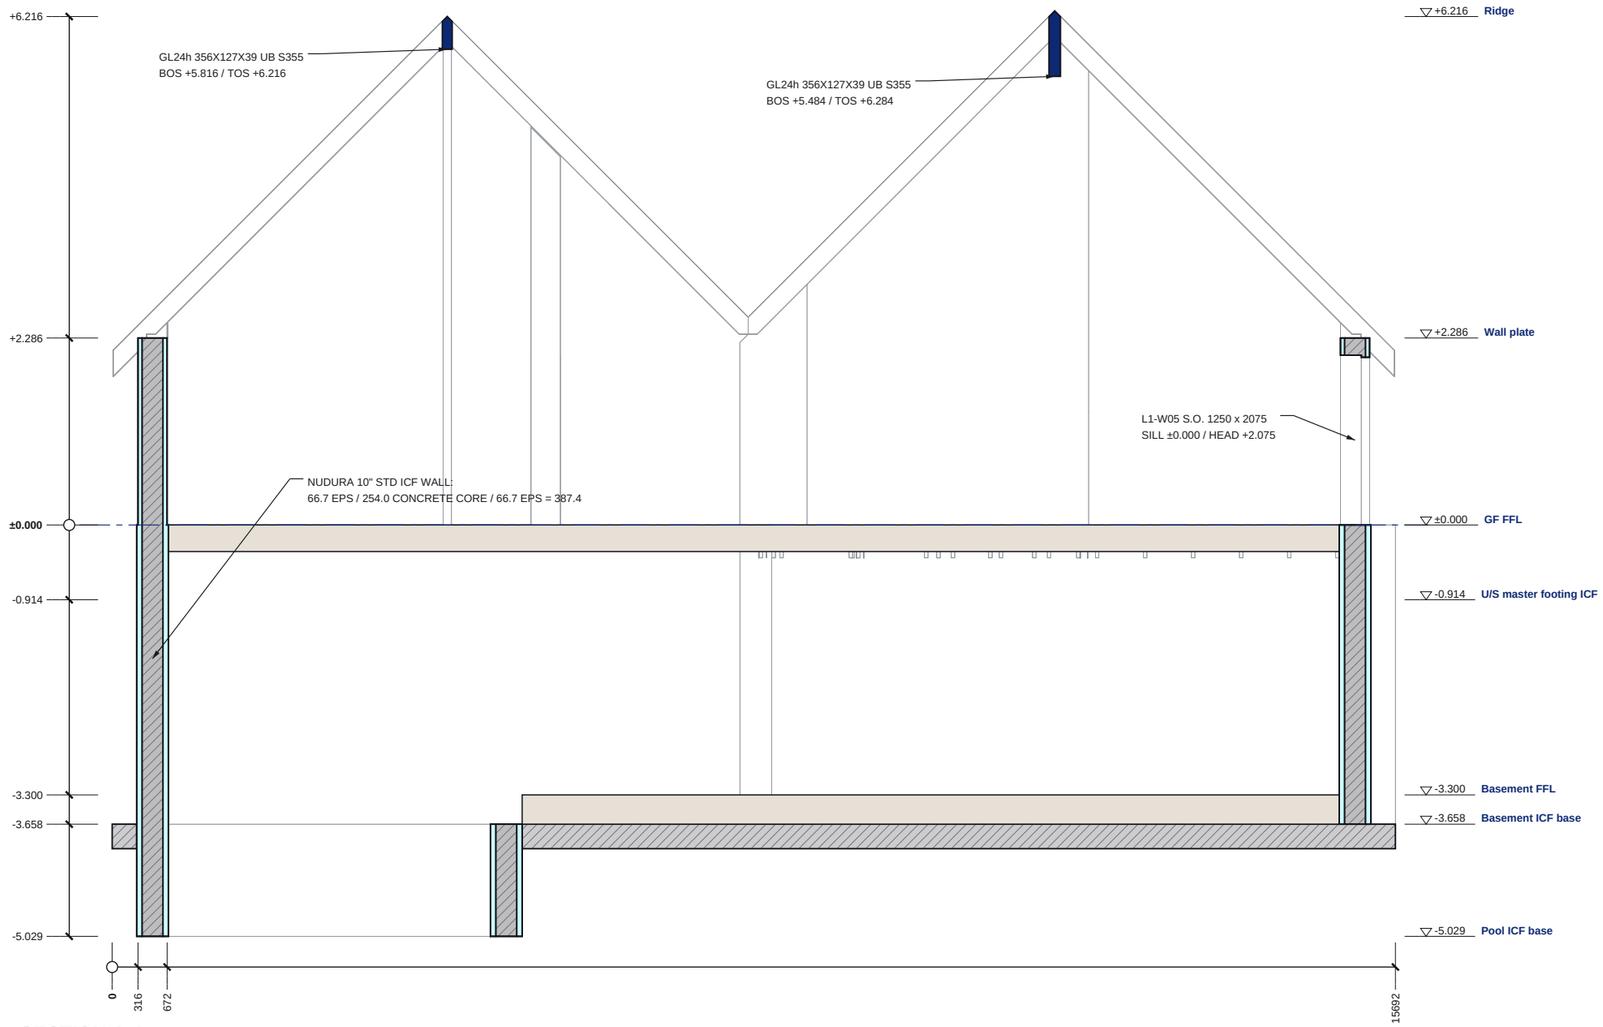

SECTION A-A

Scale 1:75 @ A3 | Looking north; levels above GF FFL

ICF EPS (cut)
ICF concrete core / RC (cut)
Steel (cut)
Beyond the cut (line work)

0 1 2 3 4m

Do not scale. All dimensions in millimetres, levels in metres from GF FFL. Check all dimensions on site.

SECTION A-A SCHEDULES


LEVELS ON THIS SECTION

Level	FFL
Pool ICF base	-5.029
Basement ICF base	-3.658
Basement FFL	-3.300
U/S master footing ICF	-0.914
GF FFL	±0.000
Wall plate	+2.286
Ridge	+6.216

STEEL CUT BY THIS SECTION

Mark	Section (engineer)	BOS	TOS
GL24h	356x127x39 UB S355	+5.816	+6.216
GL24h	356x127x39 UB S355	+5.484	+6.284

SECTION KEY

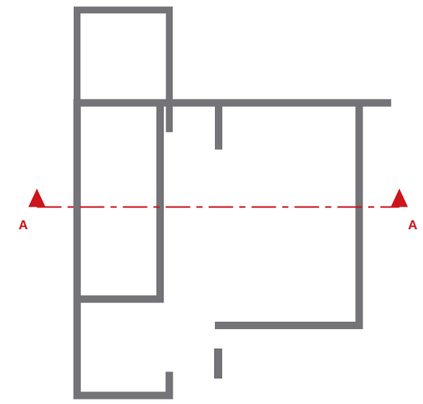

NOTES

1. Section A-A is a BuildEase ICF section (not an architect's section line). Cut elements hatched / filled; the model beyond the cut in line work.
2. Levels above GF FFL.
3. ICF: Nudura 10" Std, 66.7 EPS + 254.0 core + 66.7 EPS = 387.4; 6" XR35, 101.6 EPS + 152.4 core + 101.6 EPS = 355.6, 254.0 core + 66.7 EPS = 387.4. No structural design yet (planning drawings). ICF per the quotation model: 10in Standard pool tank + basement on the same core centre lines as the 6in XR35 ground floor; raft, pool base, GF suspended slab (pool hall + 7.5 m garage), garage door lintel, ridge beams / posts and the glazed gables for the engineer; BS 8102 waterproofing by a specialist.
4. Steel marks, BOS / TOS: rev -. See ES26-084-GA-01 / EL-01 / EL-02 in the approval drawings pack.

REVISIONS

REV	DATE	DESCRIPTION
Q01	20.10.26	First issue - proposal Rev A

Nudura™ BuildEase

CLIENT	PROJECT
Mr K & Mrs Burrell	New Dwelling, Plot 1 Rivendell Park, Douglas

DRAWING TITLE
SECTION A-A

ICF section with levels and build-ups

SCALE	SIZE	DATE
1:75	A3	20.10.26
DRAWN	CHECKED	APPROVED
TS		

STATUS	DRAWING No.	REV
QUOTATION	ES26-084-SE-01	Q01